



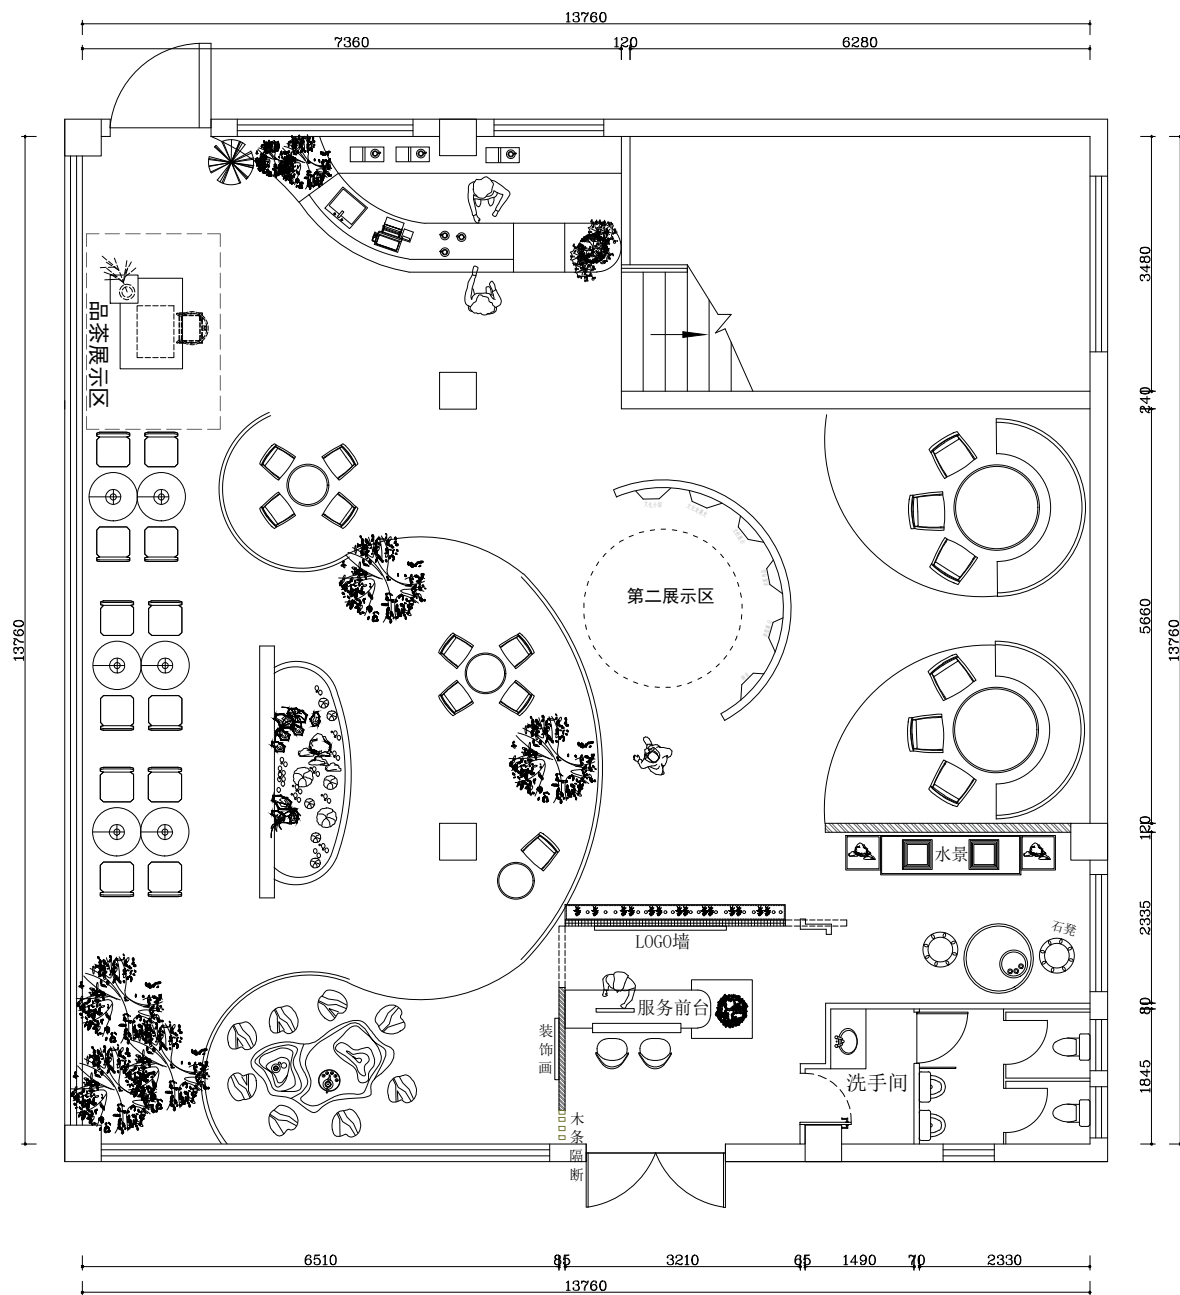

一层平面方案图




二层平面方案图

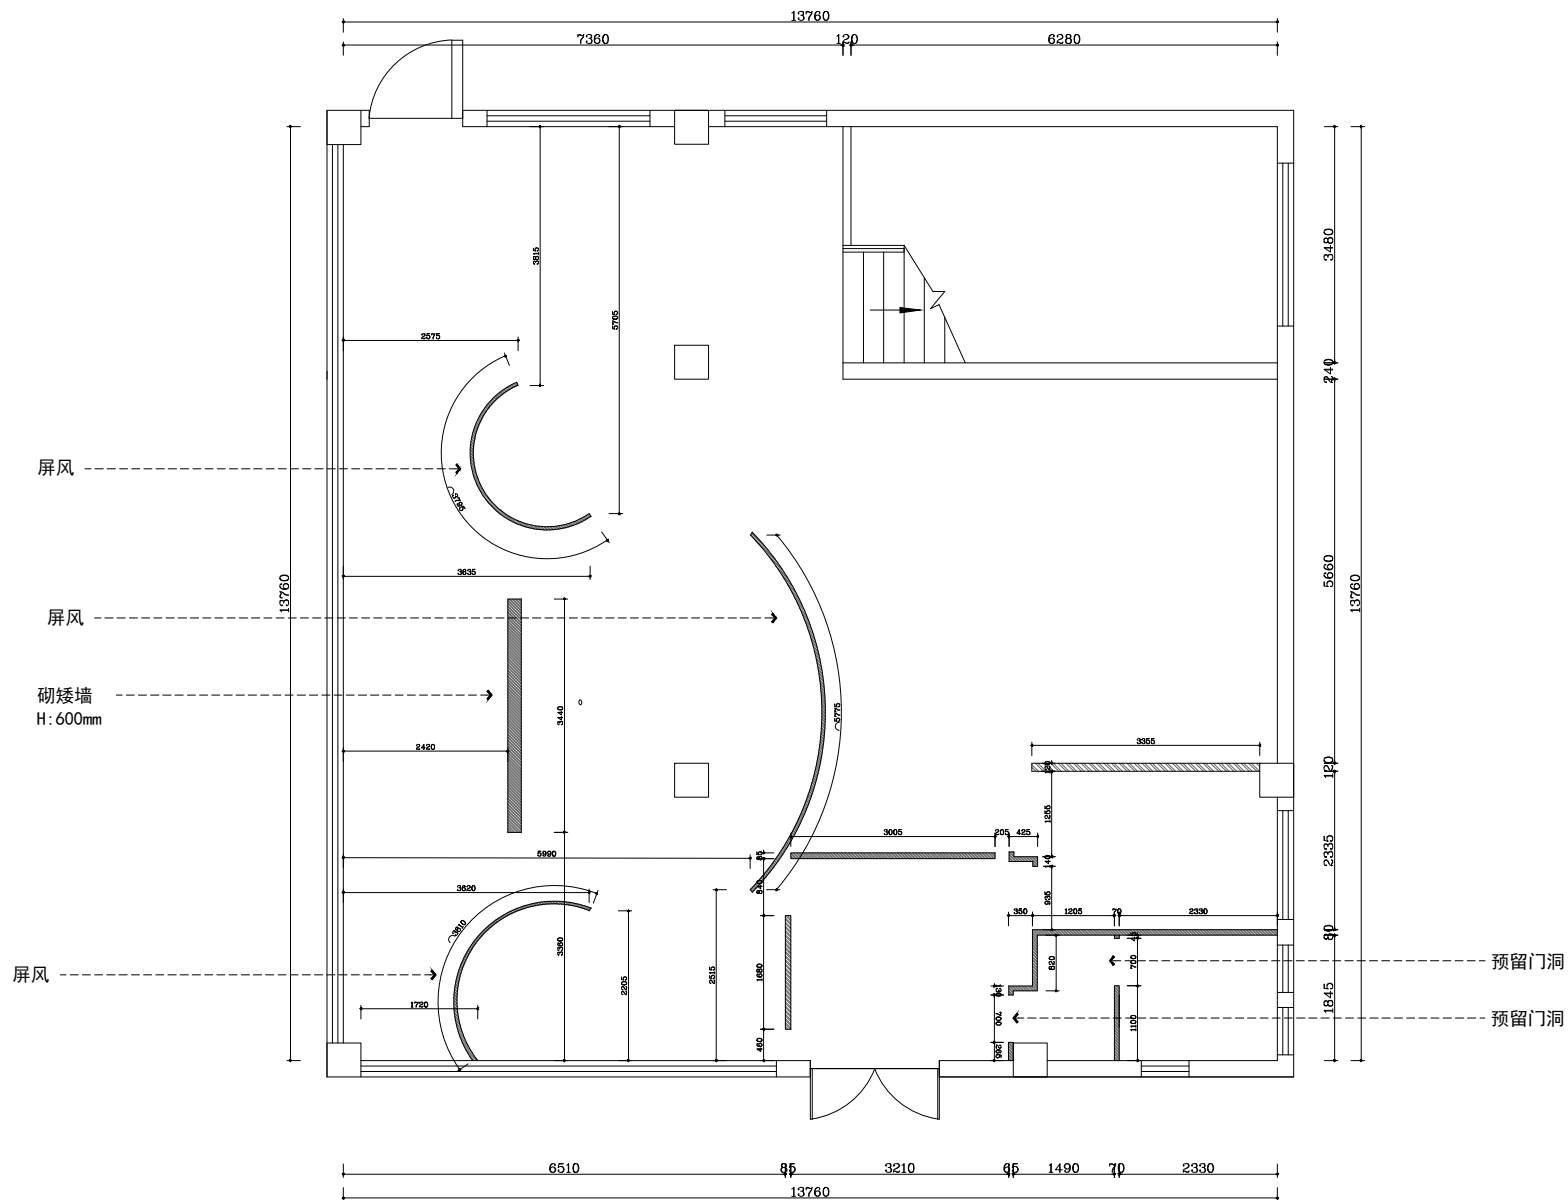


图例	说明
	墙体新建


一层建筑墙体改造图

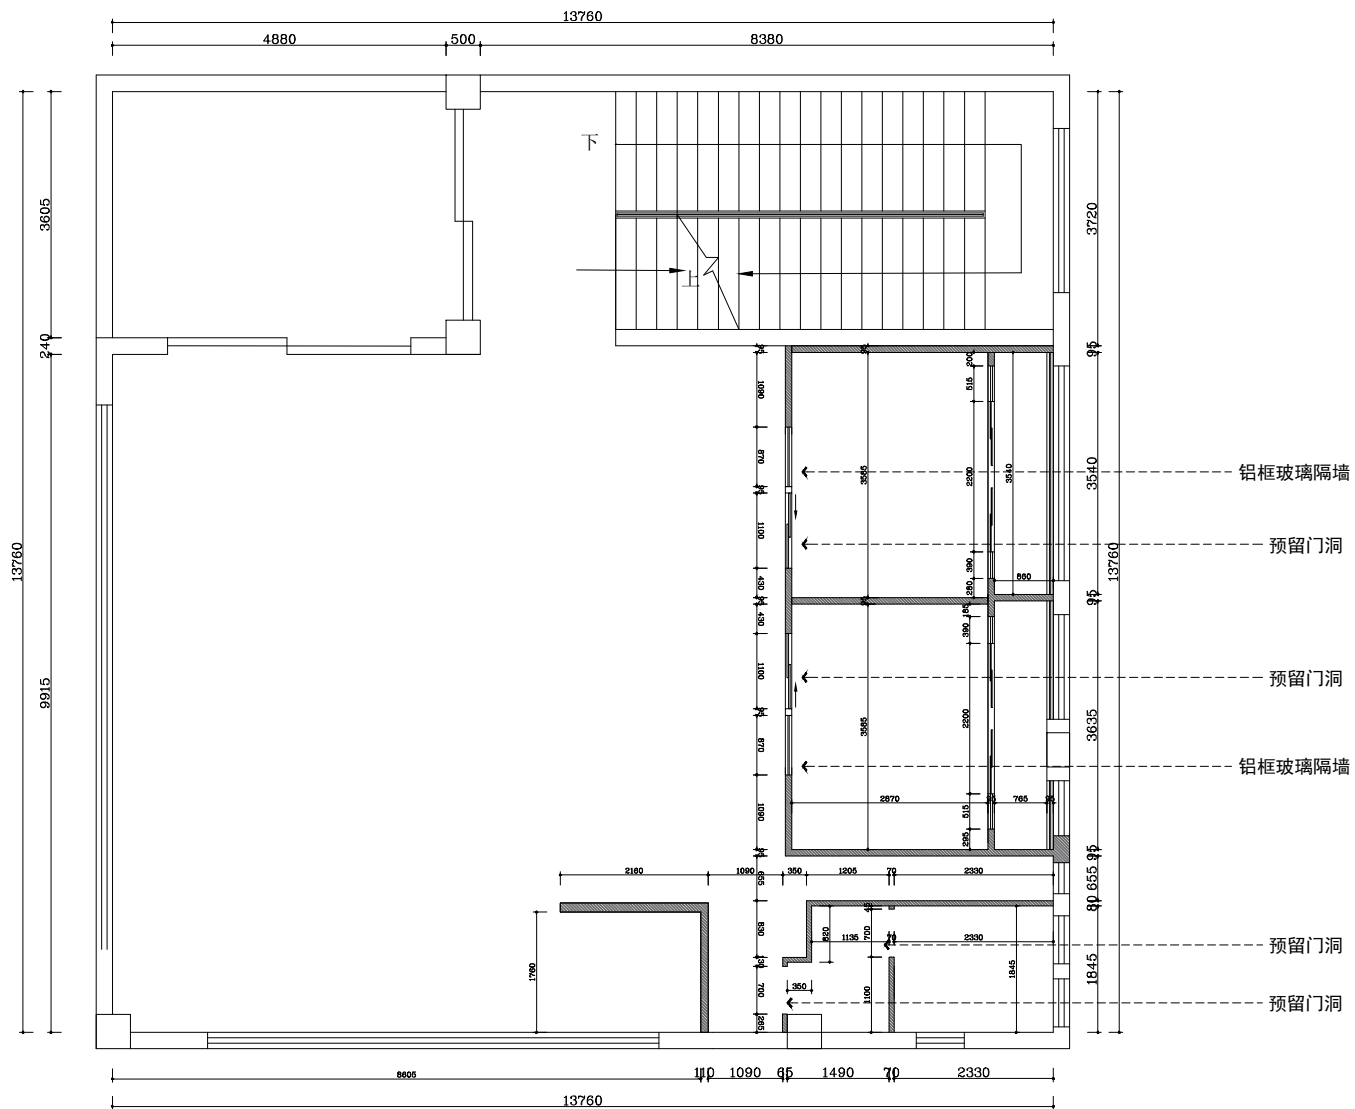

二层建筑墙体改造图

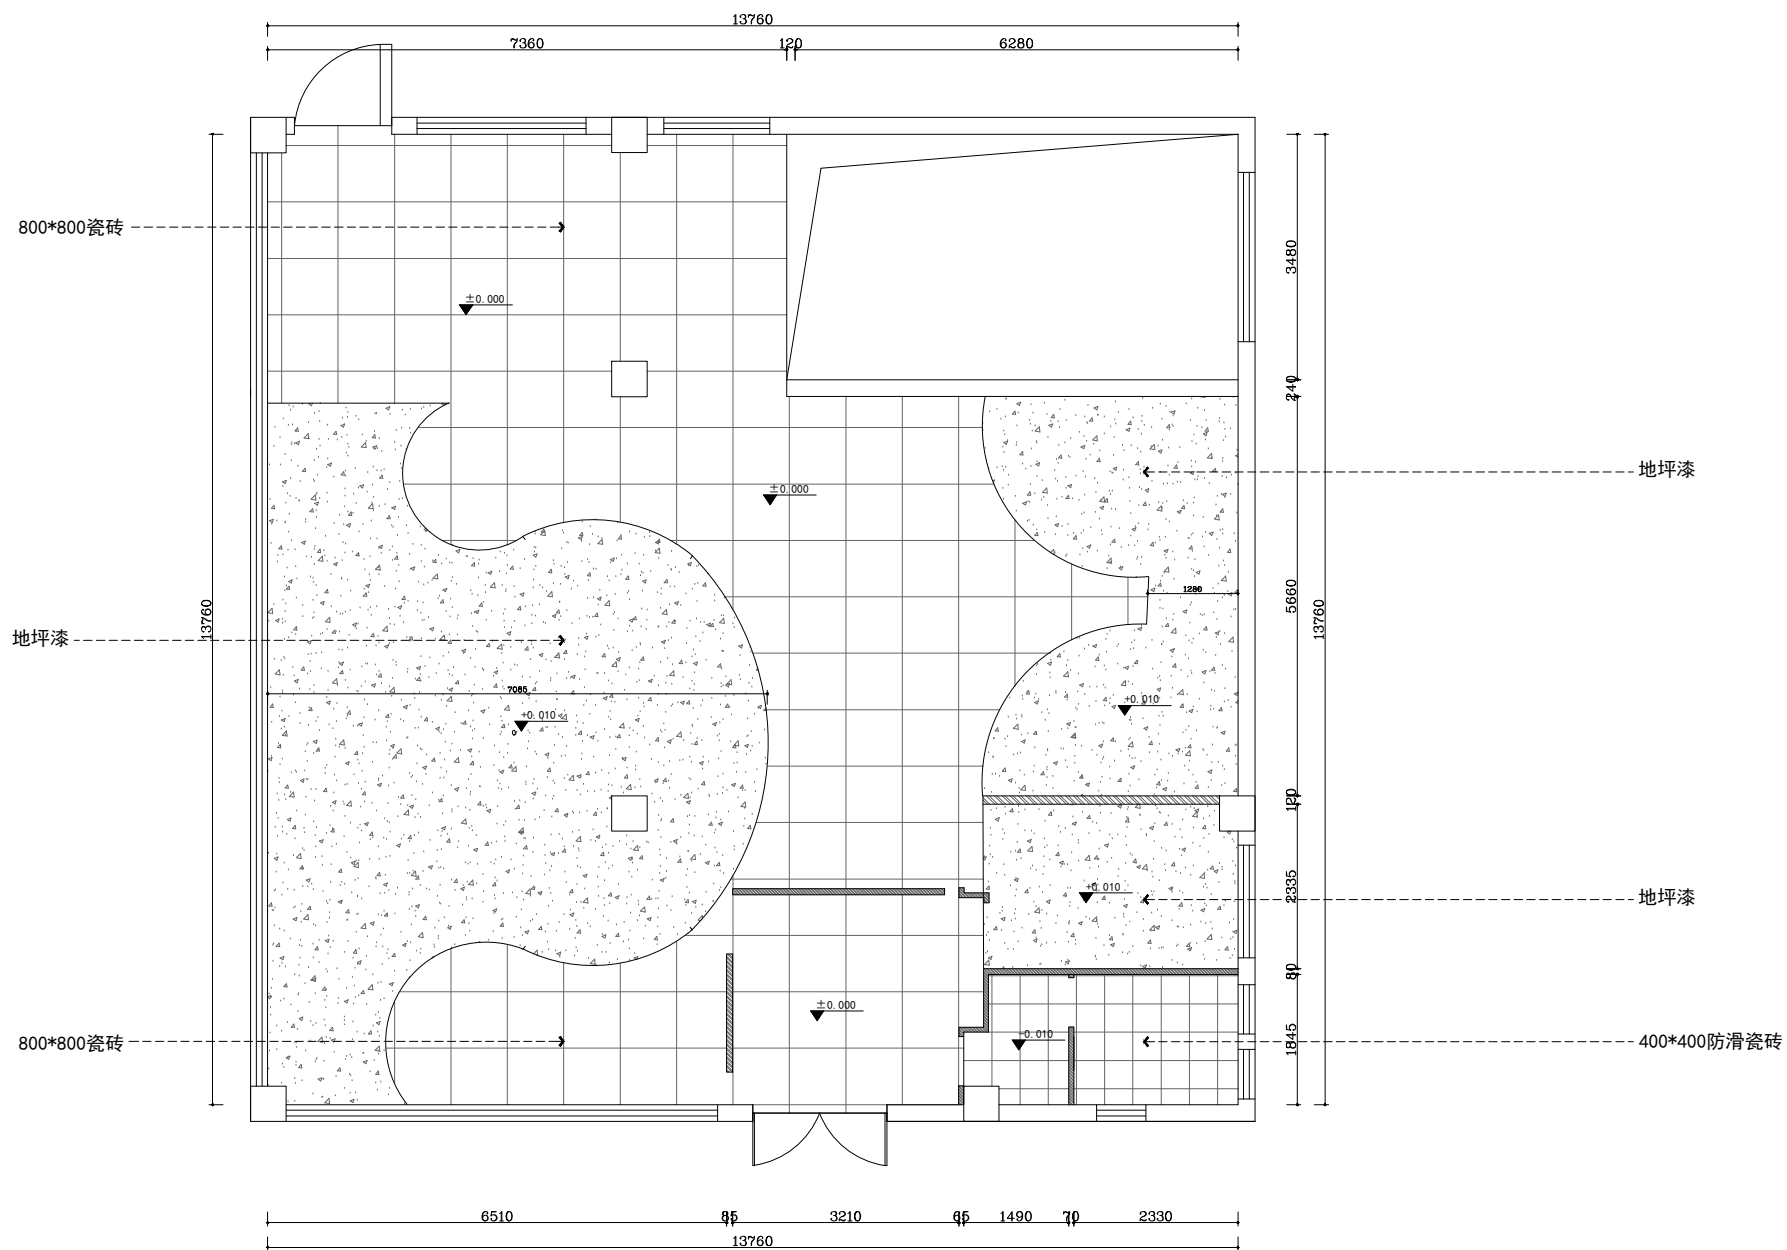


一层地面铺装图

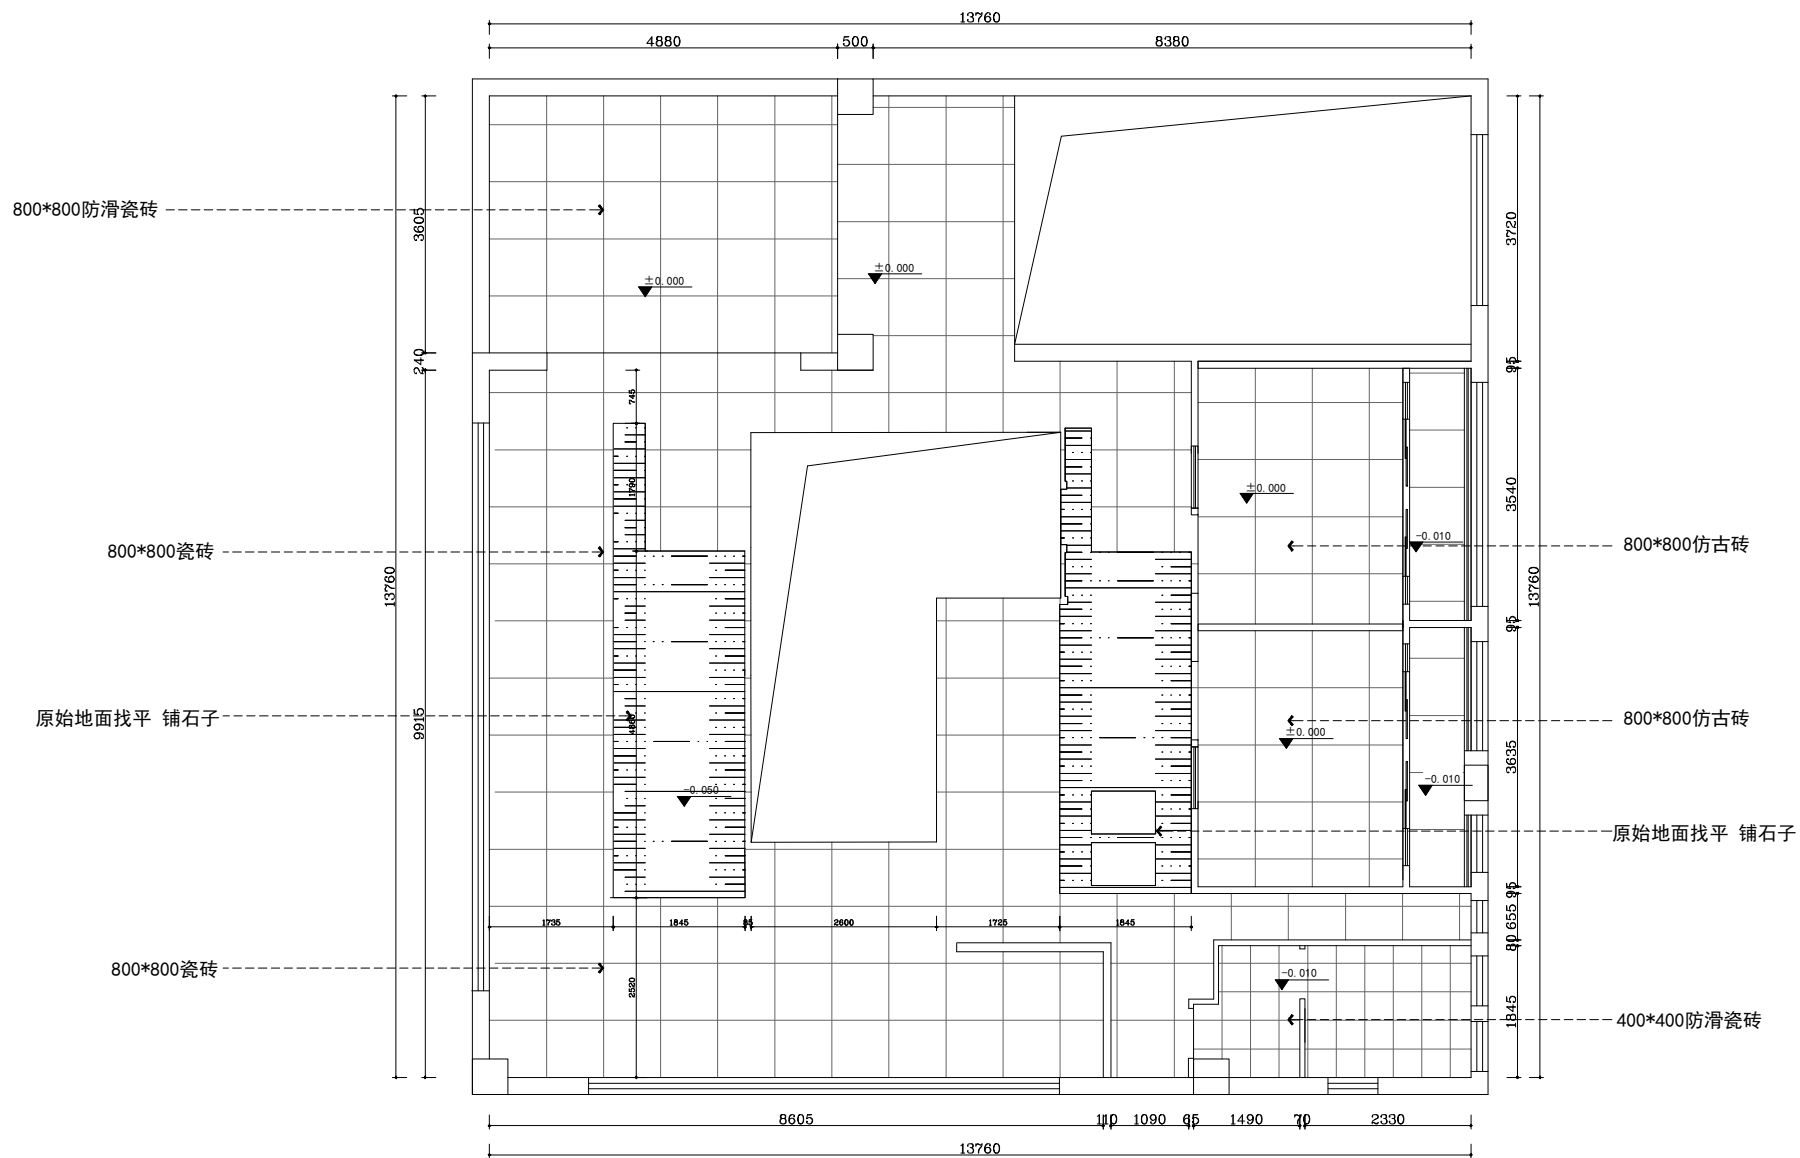


二层地面铺装图

图例说明:

序号	图例	名称
1		单相二加三孔插座
2		地面一般二加三插座
3		网络插孔
4		单联单控开关
5		双联单控开关
6		三联单控开关

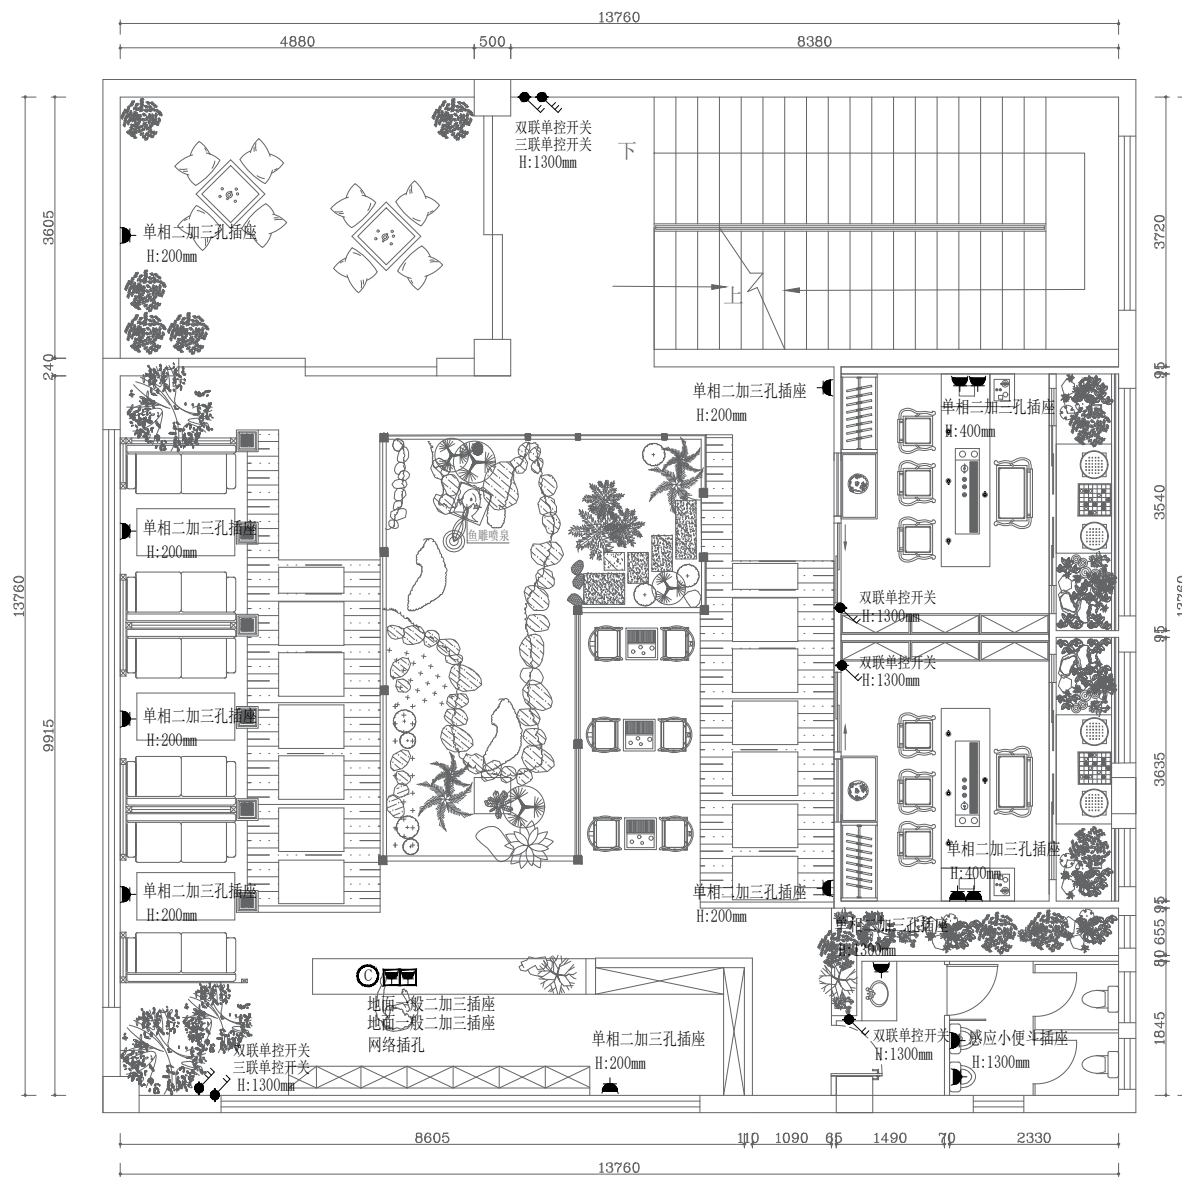


二层开关插座布置图

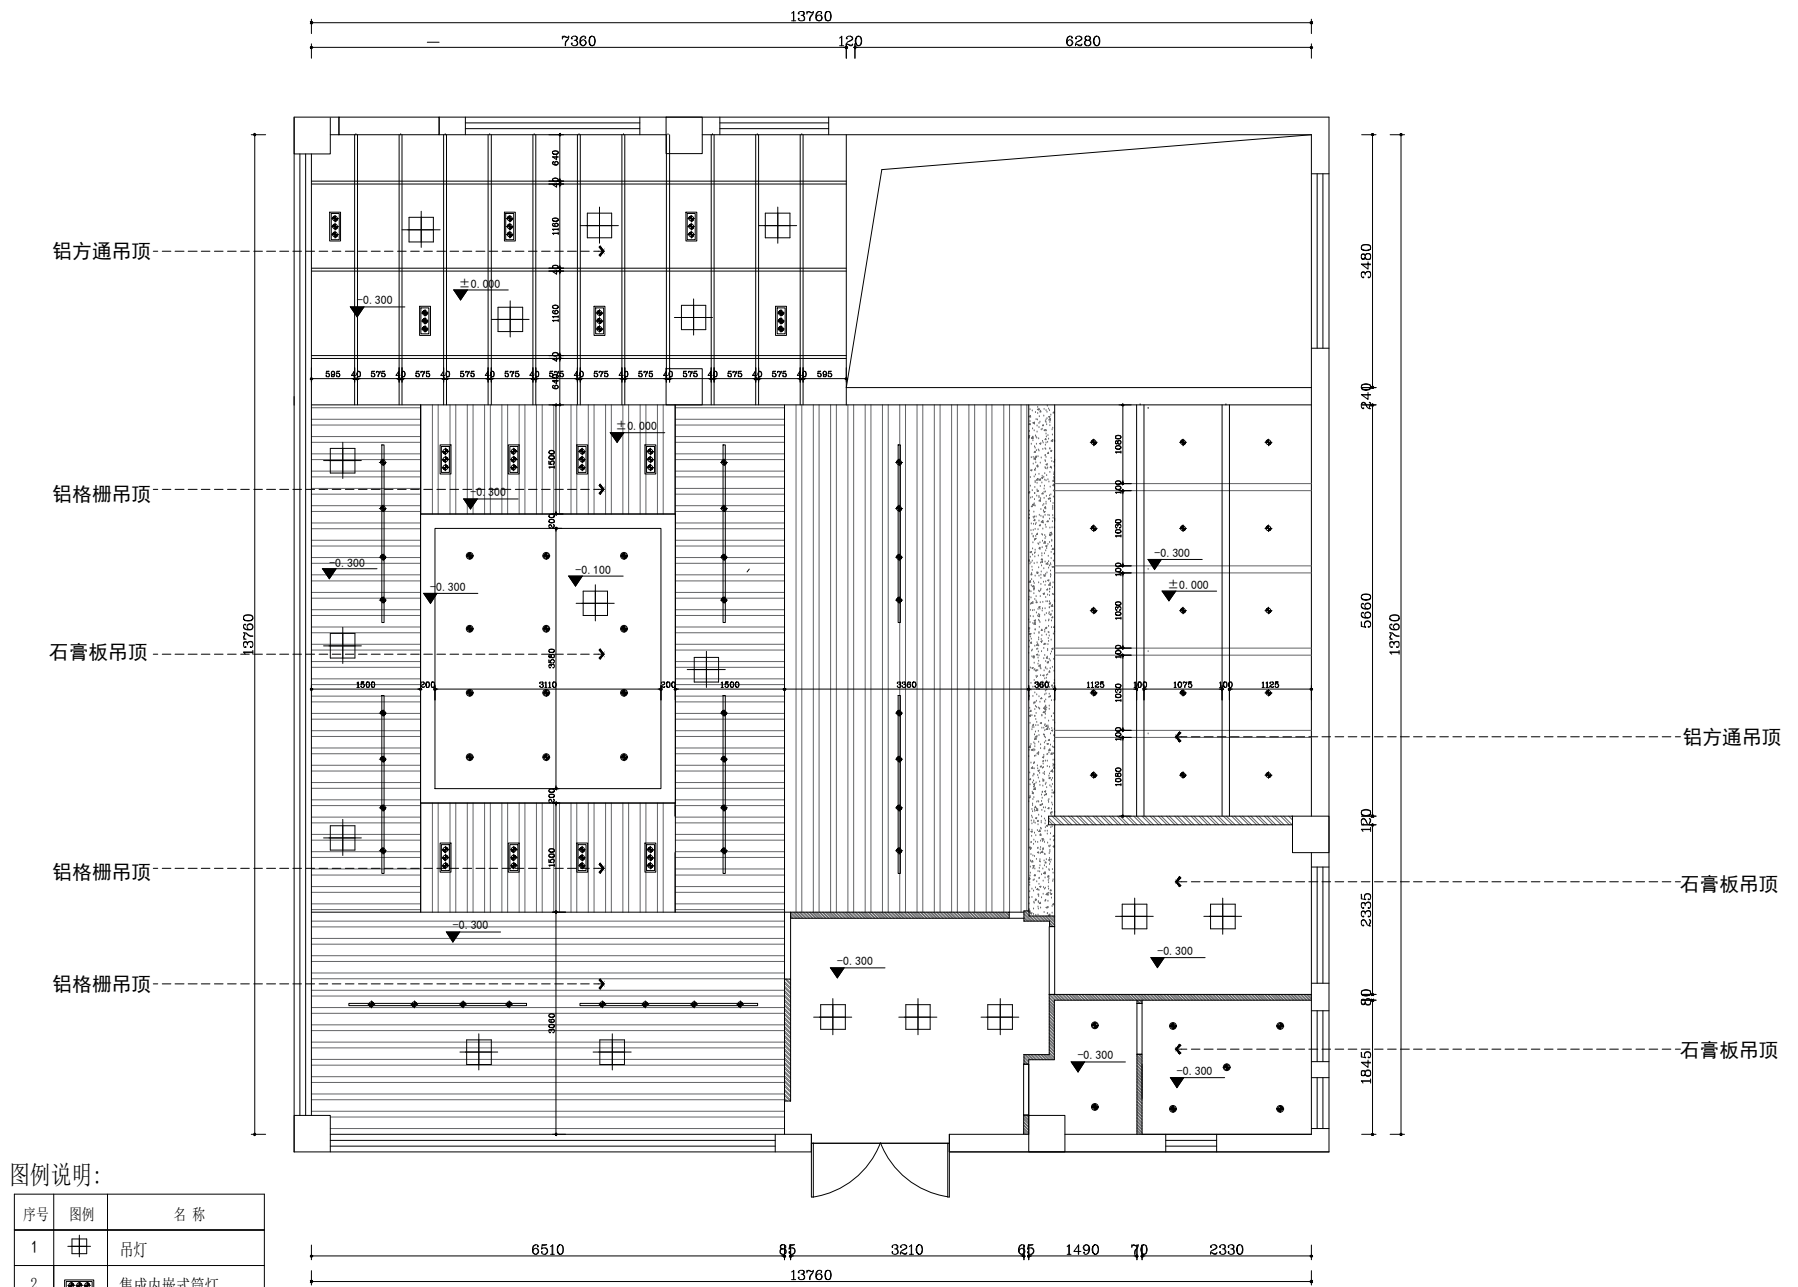

图例说明：

序号	图例	名称
1		吊灯
2		集成内嵌式筒灯
3		明装筒灯
4		内嵌式筒灯
5		轨道射灯

一层吊顶布置图

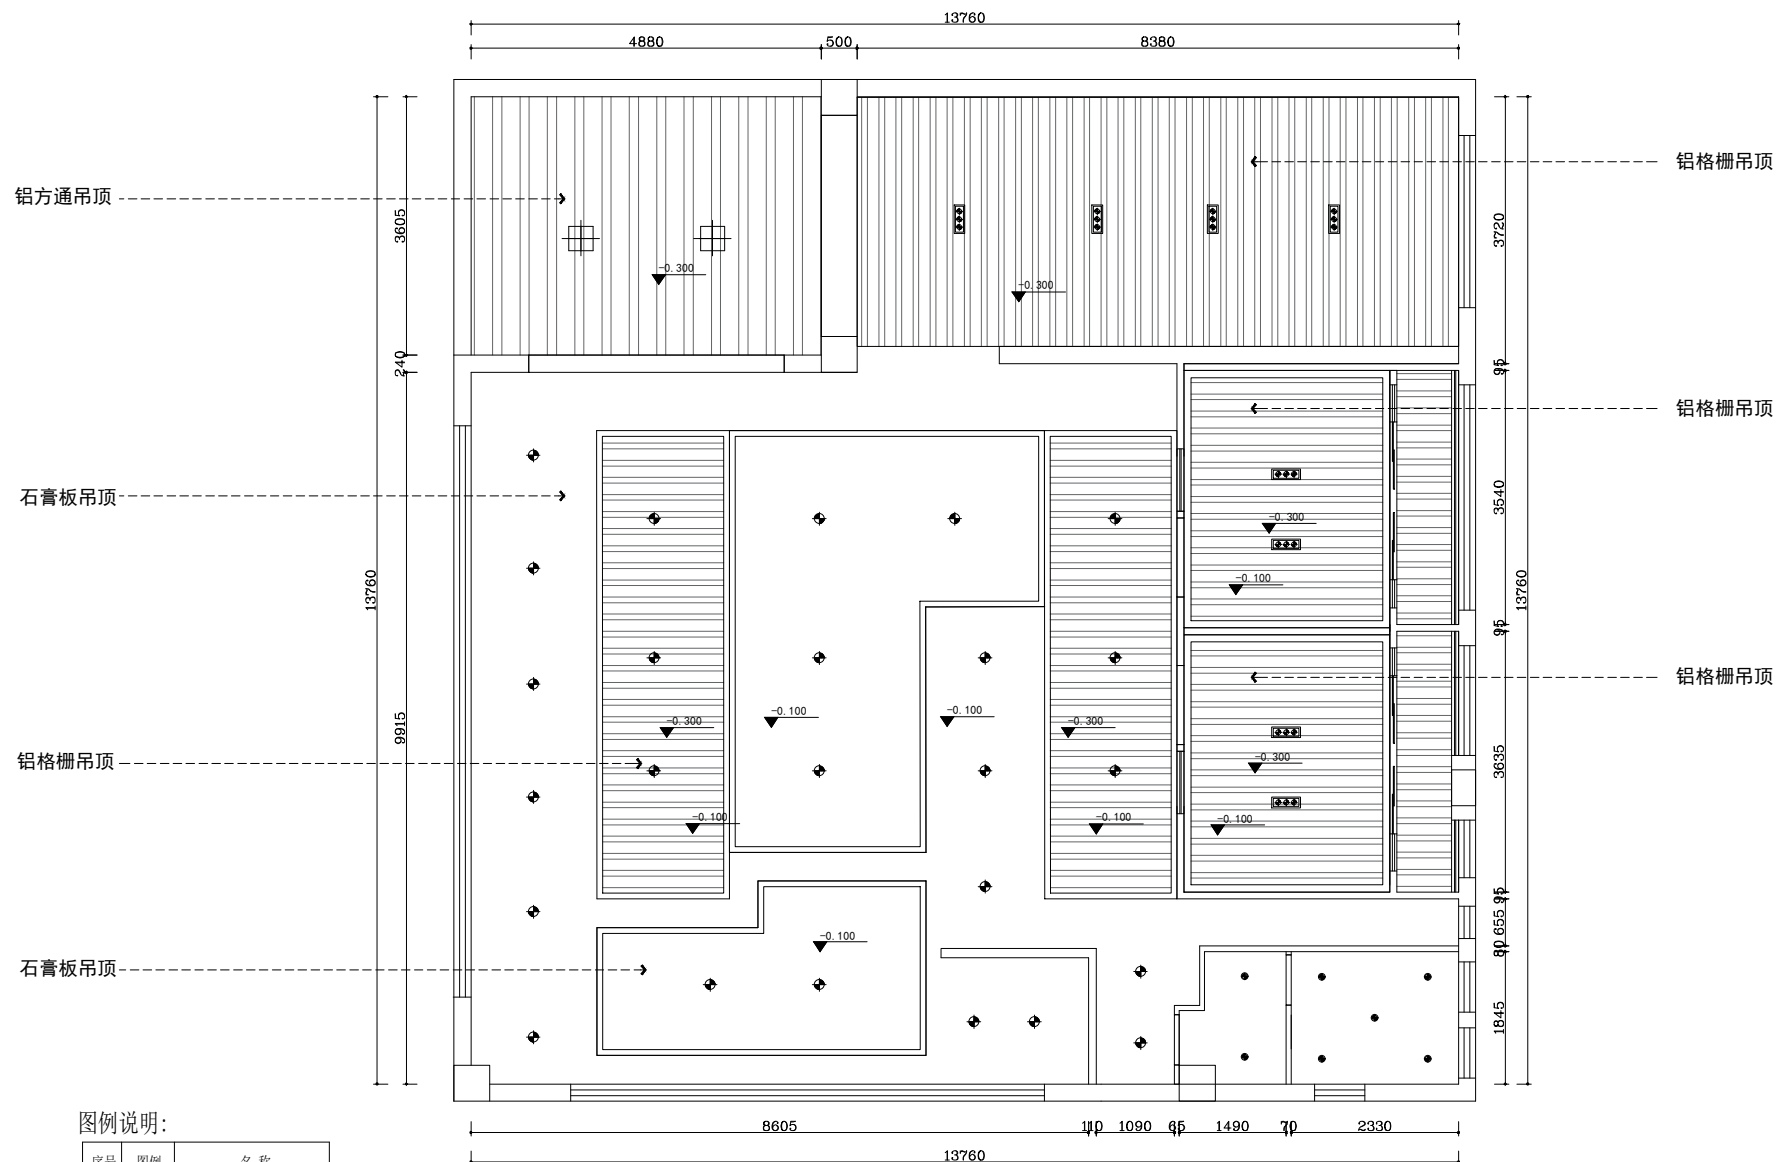

图例说明：

序号	图例	名 称
1		吊灯
2		集成内嵌式筒灯
3		明装筒灯
4		内嵌式筒灯
5		轨道射灯

二层吊顶布置图